


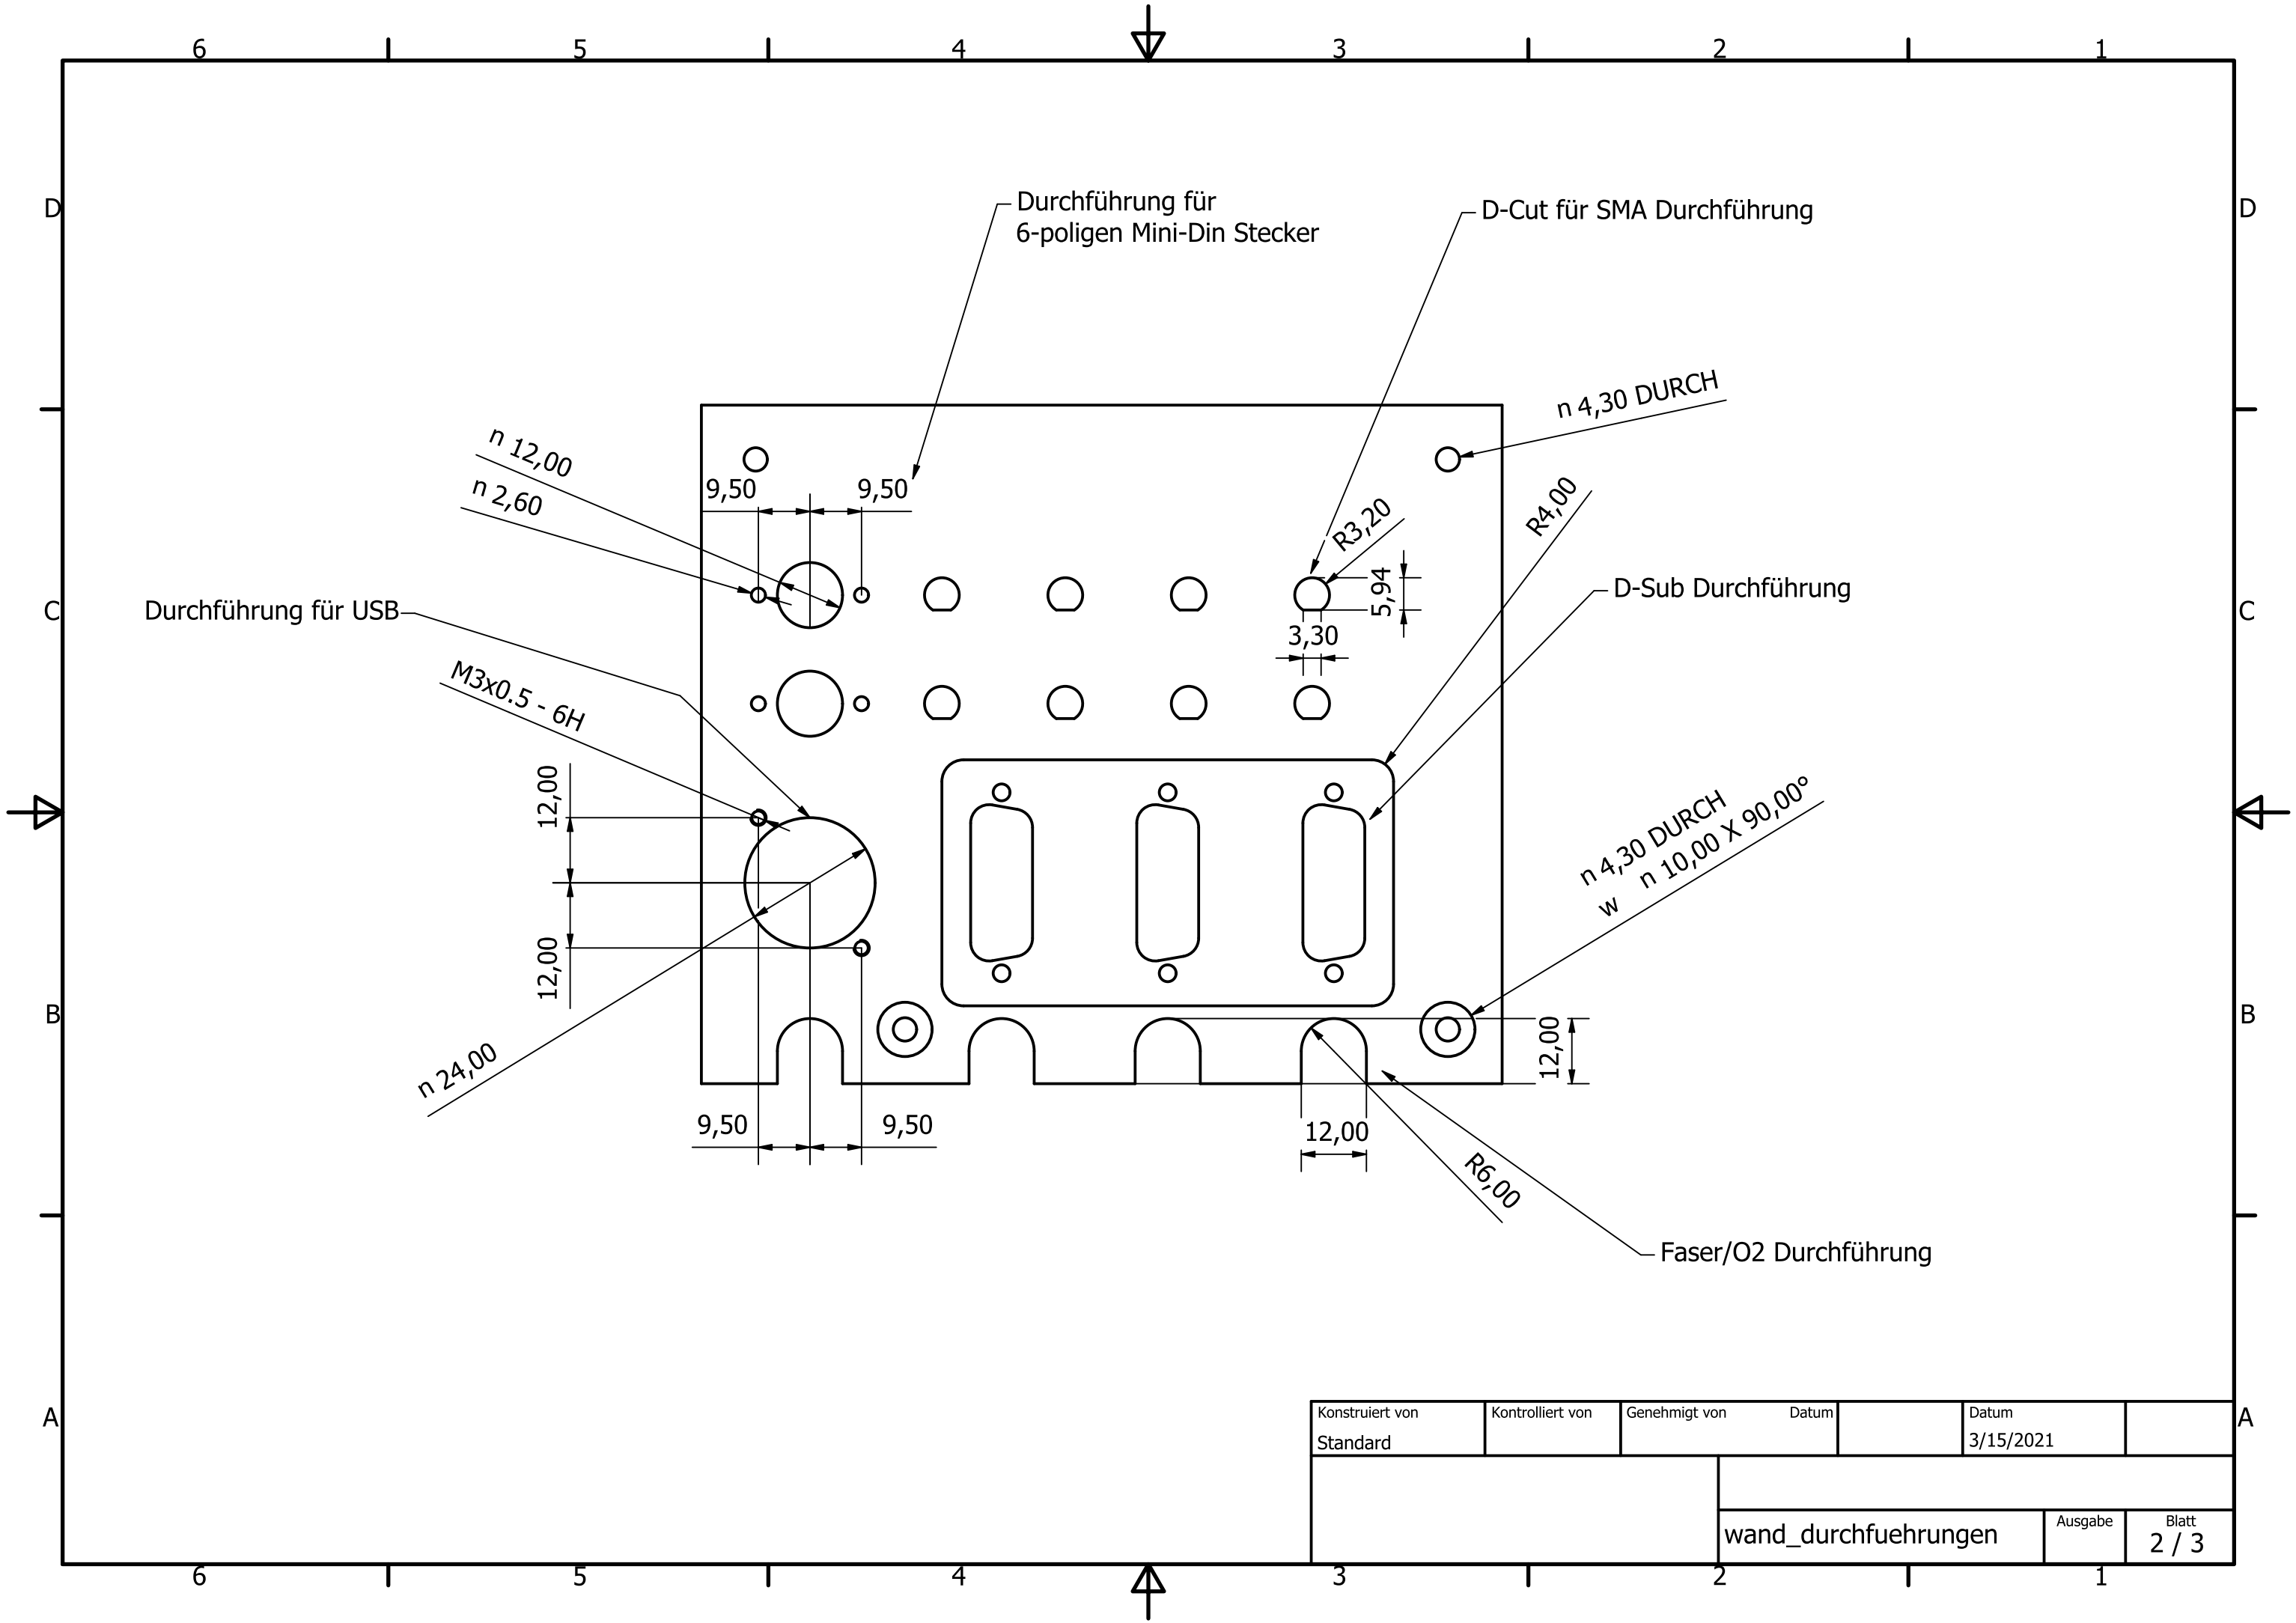

|                             |                  |               |                      |                    |                |
|-----------------------------|------------------|---------------|----------------------|--------------------|----------------|
| Konstruiert von<br>Standard | Kontrolliert von | Genehmigt von | Datum                | Datum<br>3/15/2021 |                |
|                             |                  |               |                      |                    |                |
|                             |                  |               | wand_durchfuehrungen | Ausgabe            | Blatt<br>2 / 3 |